


DETALHAMENTO DE DOBRA


Emissão: 25/06/2026 13:49
Responsável: Leonardo

Peça: Perfil U 100x20
Chapa: #18 (Esp.: 1,20 mm)
Comprimento da Peça: 3000 mm
Desenvolvimento Plano: 134 mm

DESENHO DA PEÇA

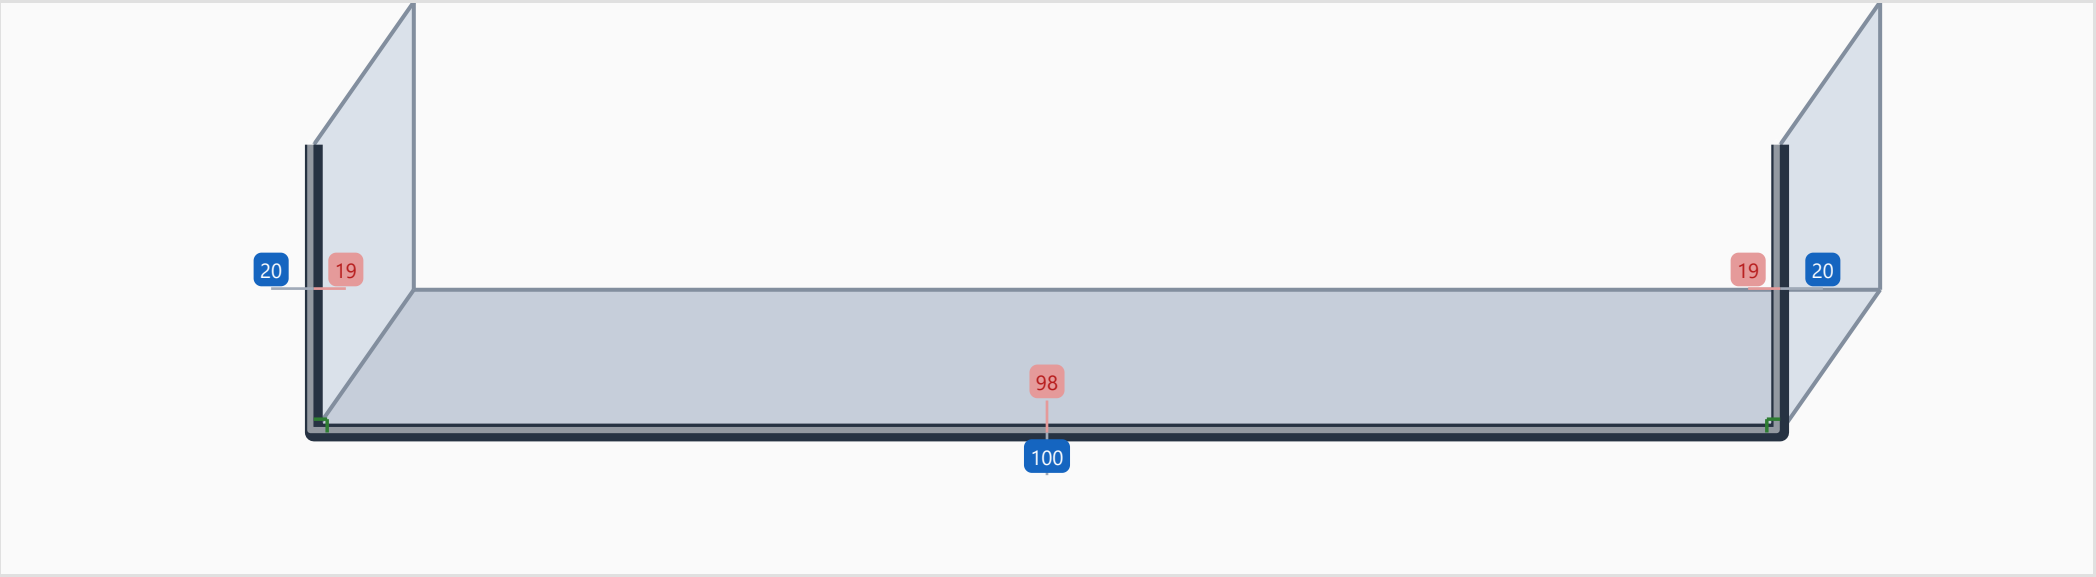

PLANIFICAÇÃO

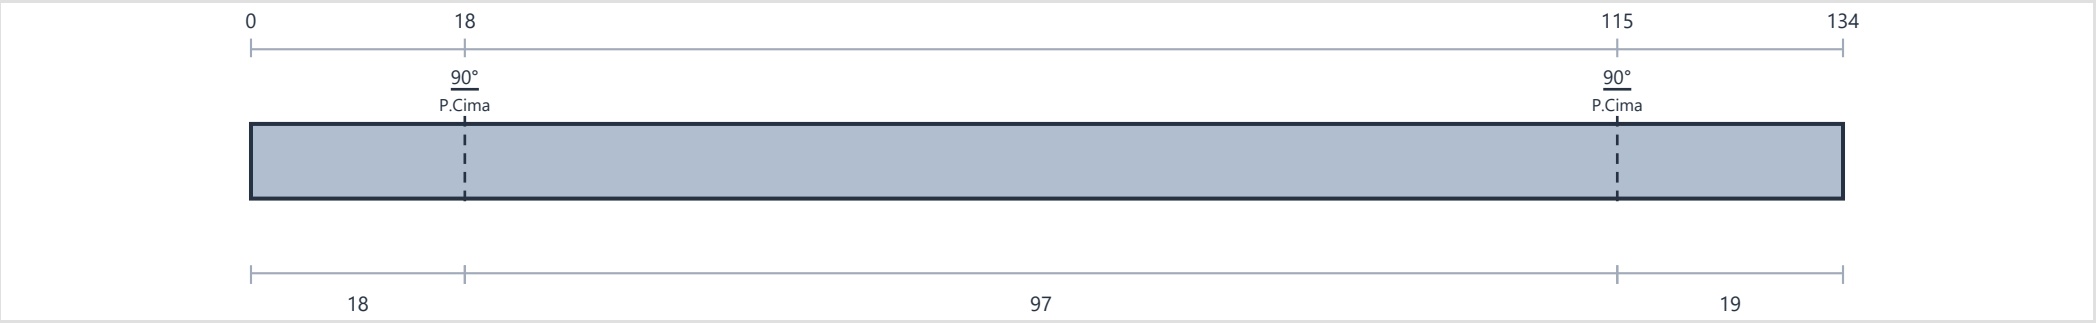

Legenda: fundo escuro/letra branca = medida externa · fundo claro/letra escura = medida interna · ângulo sublinhado = dobra não-reta · linha tracejada = dobra p/ cima · linha contínua = dobra p/ baixo
Cotas no topo da planificação = acumuladas desde o início da chapa · cotas na base = entre dobras sucessivas